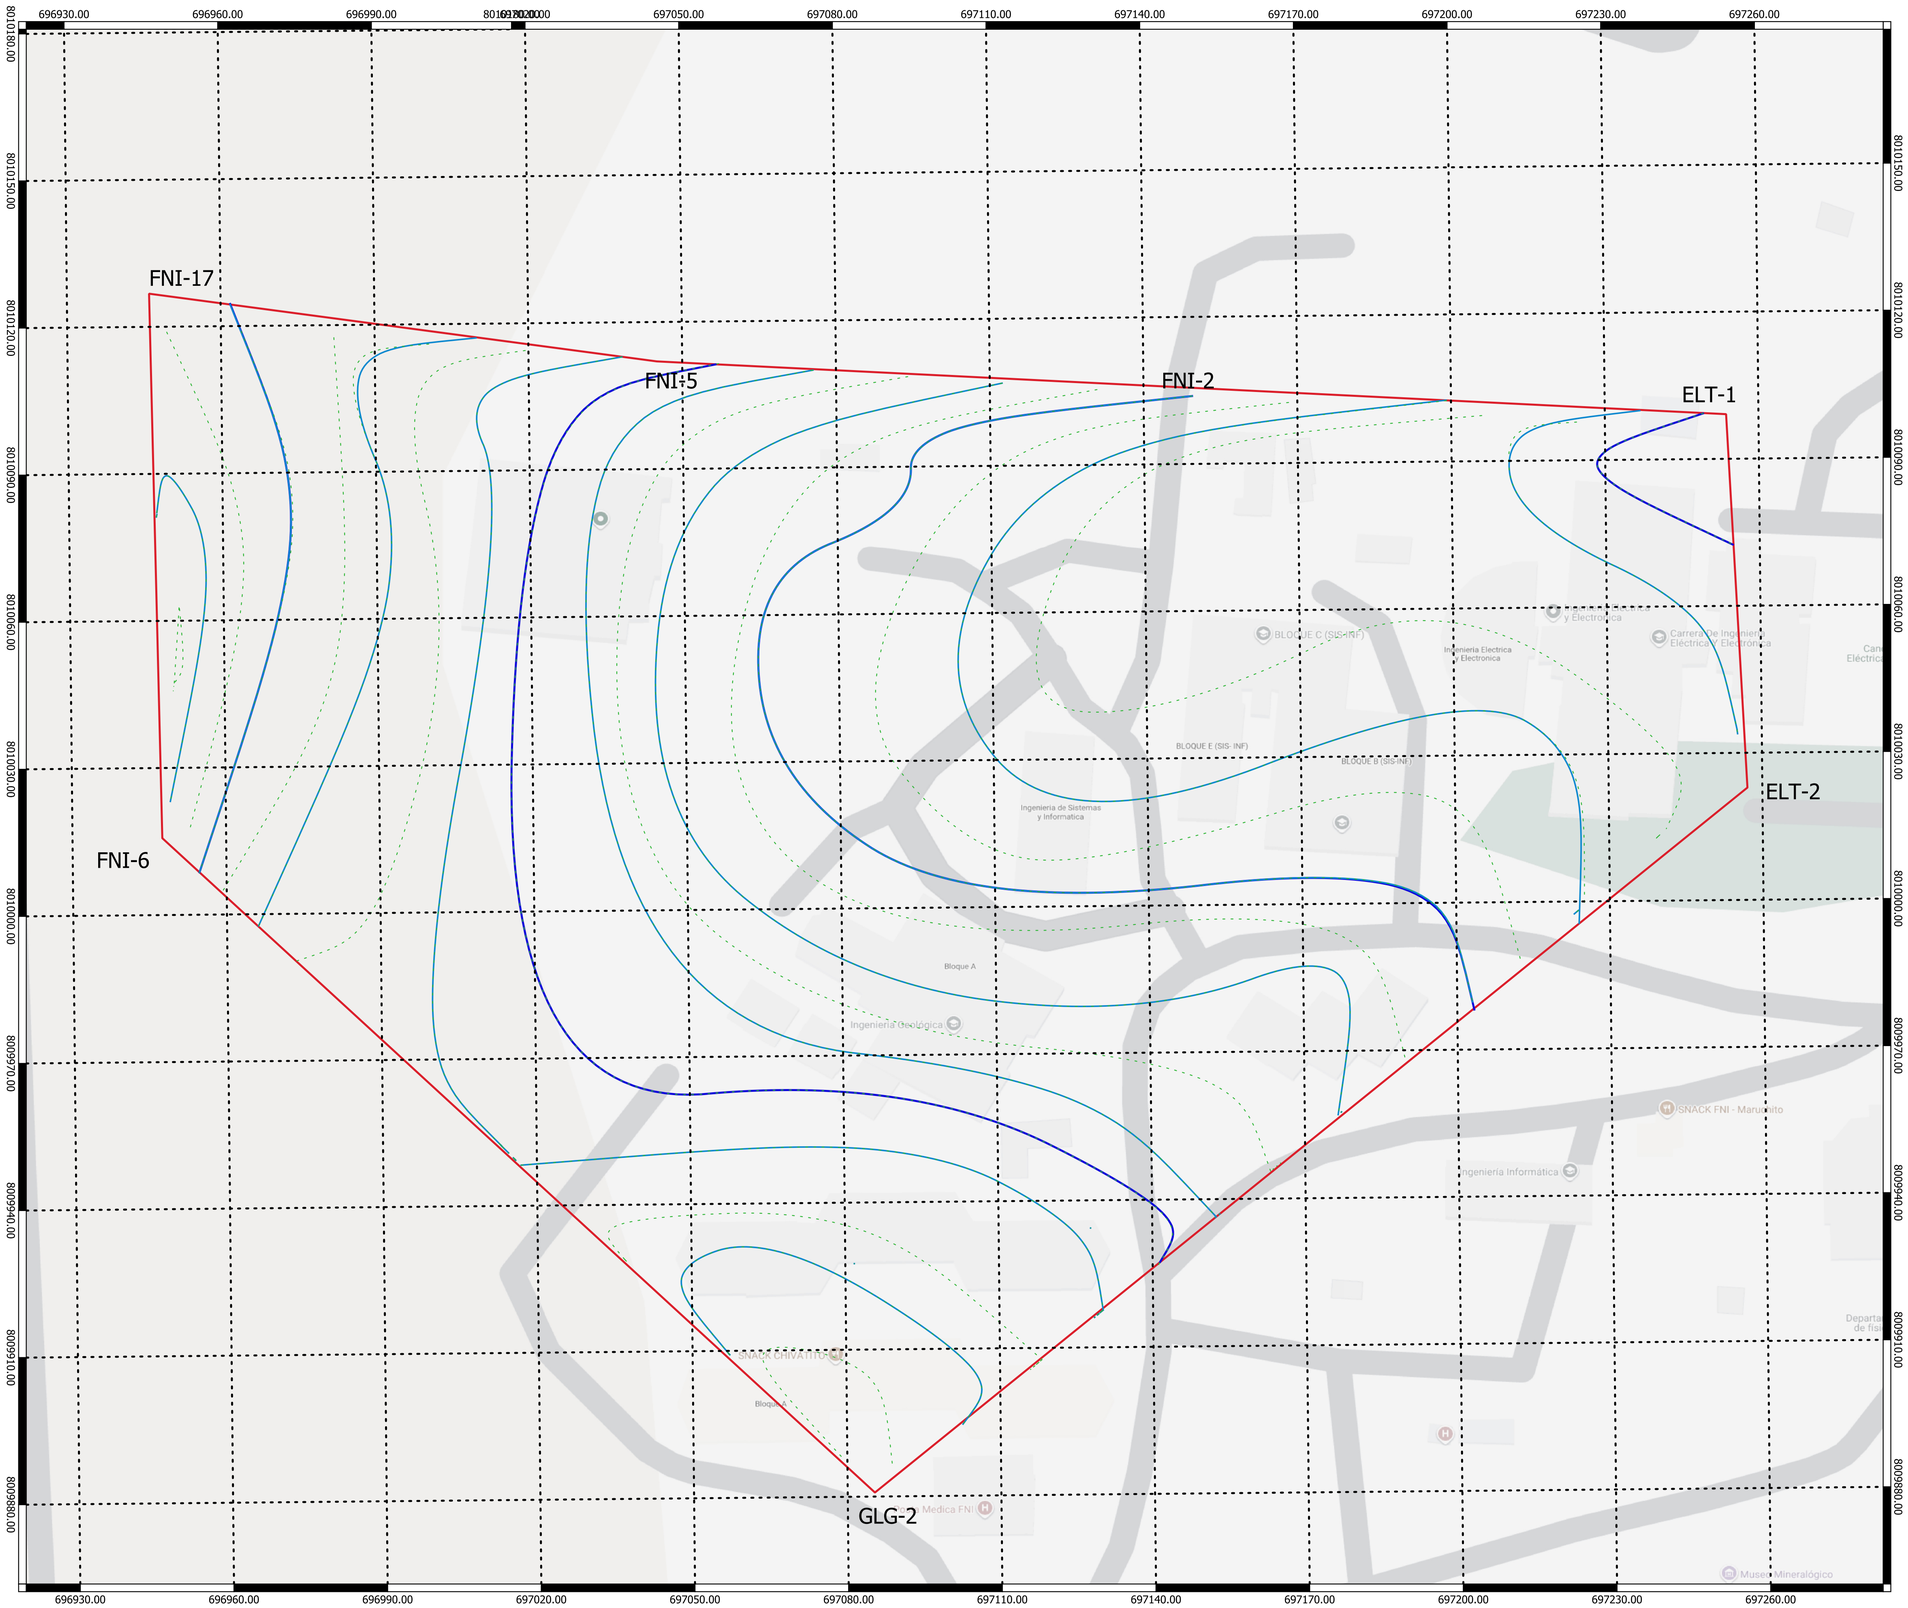


0 25 50 75 100 125 m

ESC: 500

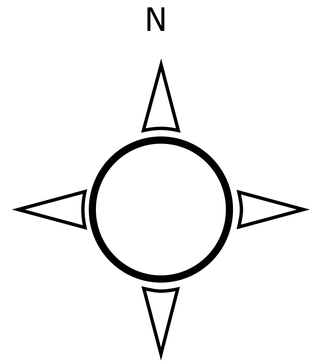


Curvas3

Curvas2

Curvas1

Interpolado

Banda 1 (Gray)

3.743

3.725

Polyline

Puntos

Google Road

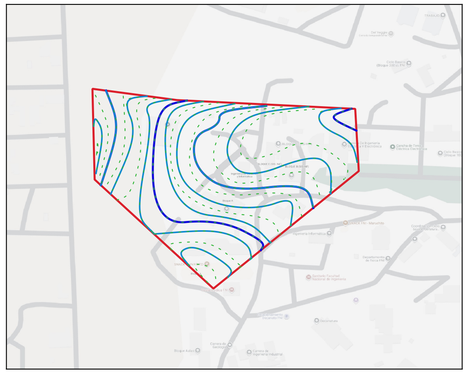

ESC: 3000

| | | | |
|---|---|---|---|
| UNIVERSIDAD TECNICA DE ORURO<br>FACULTAD NACIONAL DE INGENIERIA<br>INGENIERIA CIVIL | | NOMBRES : | |
| | | DOCENTE : | Ing. Armando Garnica Medinaceli |
| | | AUXILIAR : | Univ. Mauricio R. Luna Vasquez |
| TOPOGRAFIAI | CIV : 2214-'B' | ALUMNO : | UNIVI: TRUJILLANO CHOQUE FRANZ GROVER |
| TRABAJO | NIVELACIÓN DE BANCOS DE NIVEL | | HOJA 1/1 |
| | | | CALIFI. |
| ESCALA : 1 : 500 | FECHA: | DIBUJO 06/04/2026 | ENTREGA 06/04/2026 |