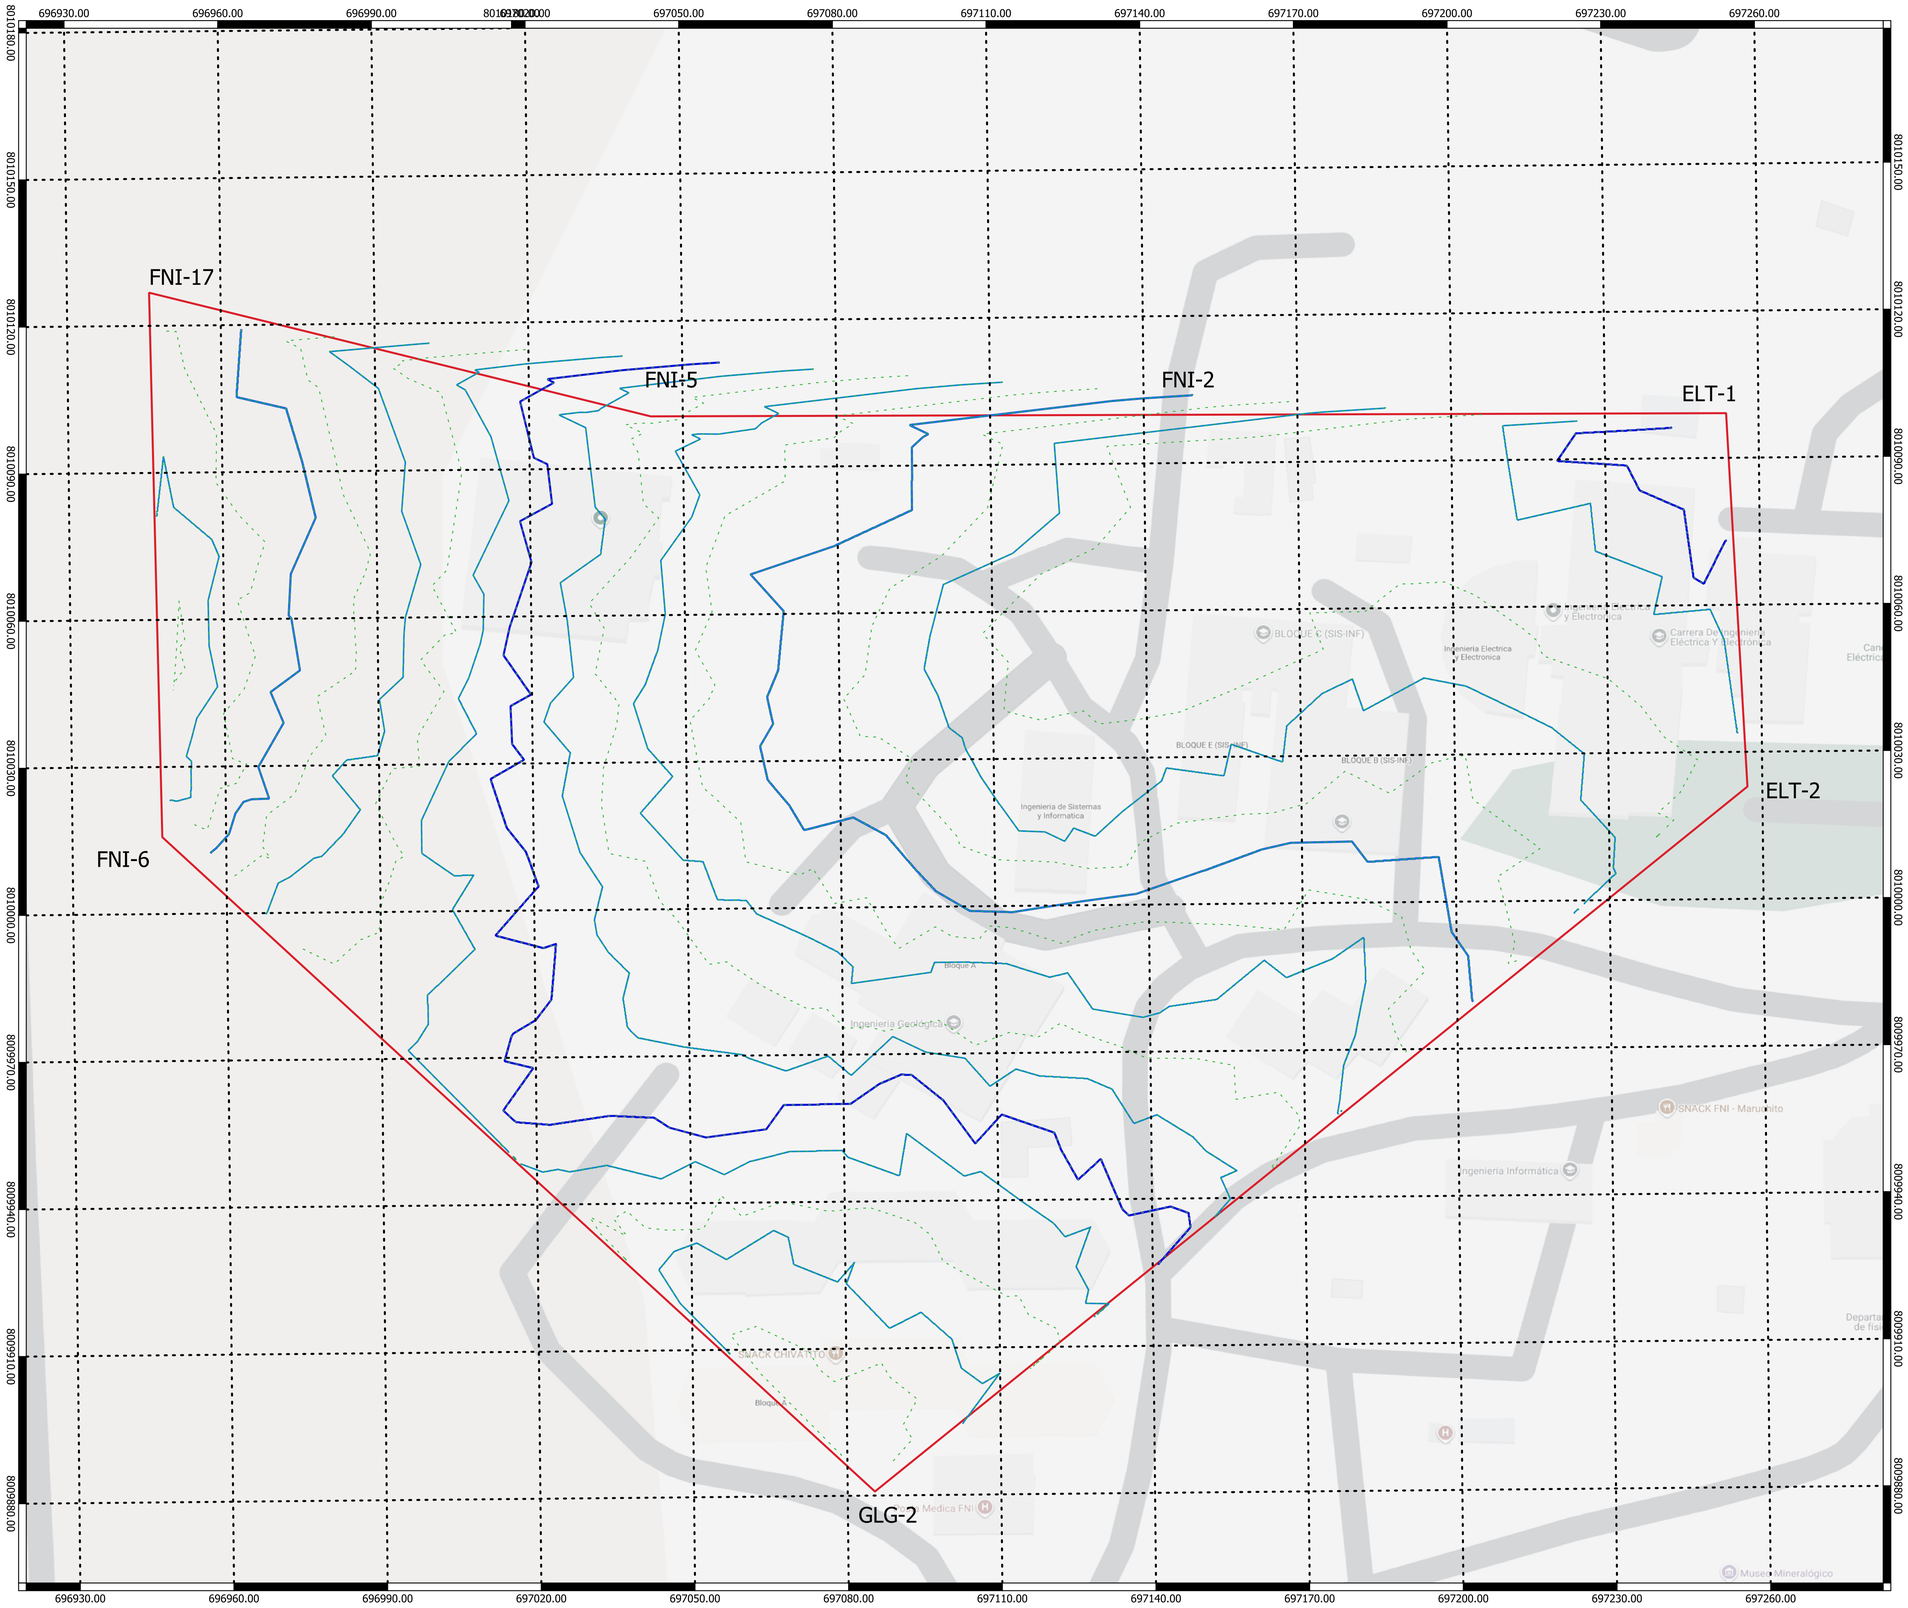

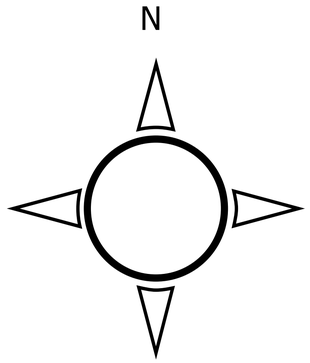

Curvas3

Curvas2

Curvas1

Interpolado

Banda 1 (Gray)

3.743

3.725

Polyline

Puntos

Google Road

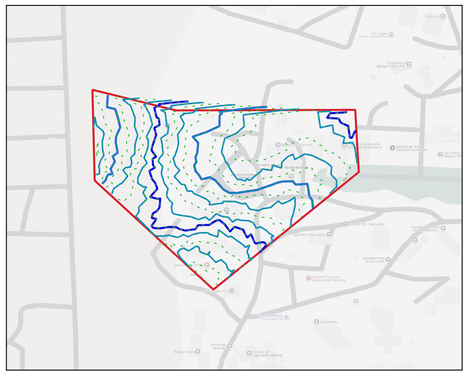

ESC: 3000

0 25 50 75 100 125 m

ESC: 500

UNIVERSIDAD TECNICA DE ORURO FACULTAD NACIONAL DE INGENIERIA INGENIERIA CIVIL		NOMBRES :	
		DOCENTE :	Ing. Armando Garnica Medinaceli
		AUXILIAR :	Univ. Mauricio R. Luna Vasquez
TOPOGRAFIA I	CIV : 2214-'B'	ALUMNO :	UNIV: TRUJILLANO CHOQUE FRANZ GROVER
TRABAJO	NIVELACIÓN DE BANCOS DE NIVEL		HOJA 1/1
			CALIFI.
ESCALA : 1 : 500	FECHA:	DIBUJO 06/04/2026	ENTREGA 06/04/2026